


Entered in tract book 3
Vol 3, page 373
CHS 3

Township No 4 South, Range No 2 West Willamette Meridⁿ

OREGON

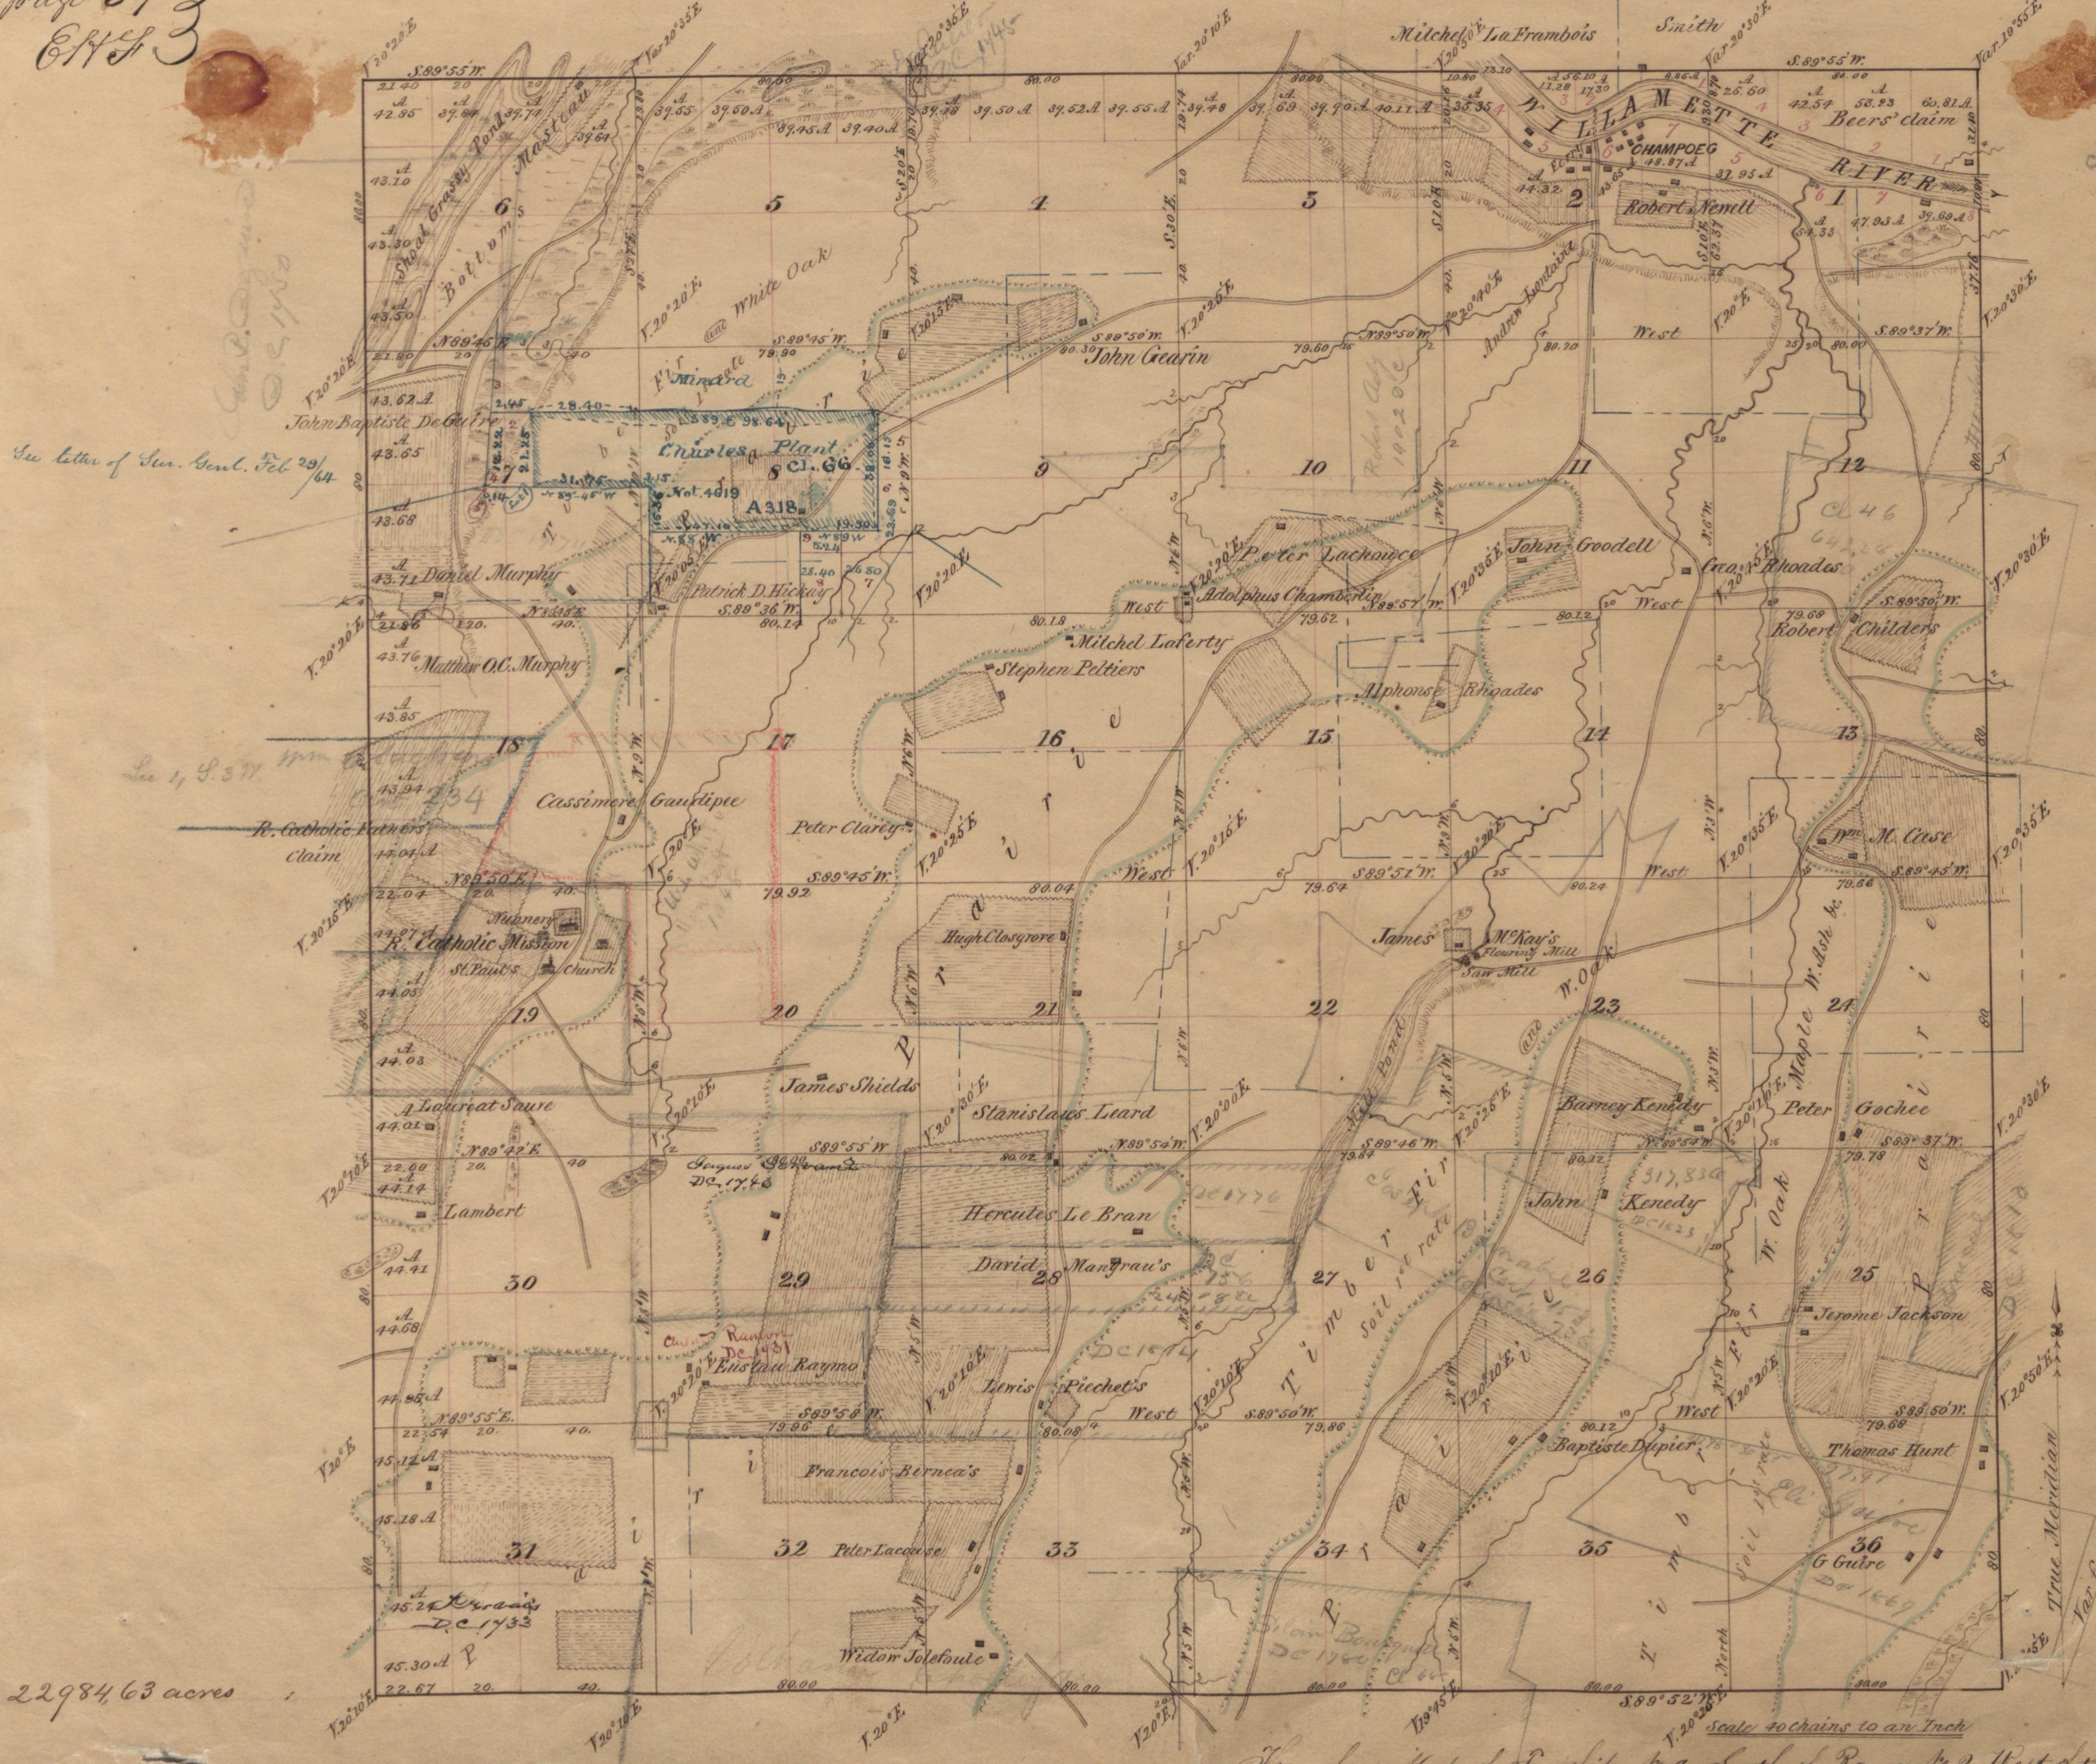

Surveys Designated By Whom Surveyed	Contract No	Date	Amount of Surveys Miles Chain Lbs	When Surveyed	When Charged in the Surv. Genl's account
Township Lines	William Jones	12 Mar 25 th 1852	12 2 67	May 20 th 1852	2 ^d Quarter 1852
Subdivisions	W. Jones	18 May 21 st 1852	63 72 61	June 30 th 1852	2 ^d Quarter 1852

POOR COPY

The above Map of Township No 4 South of Range No 2 West of the Willamette Meridian Territory of Oregon is strictly conformable to the field notes of the Survey thereof on file in this Office, which have been examined and approved
Surveyor General's Office
City of June 30th 1852